


SECS. 11-12-13-14-24,
T. 1 N., R. 8 E.
UNSUR.
SEC. 18,
T. 1 N., R. 9 E.
UNSUR.

SEE SHEET 2 FOR CANCELLATIONS

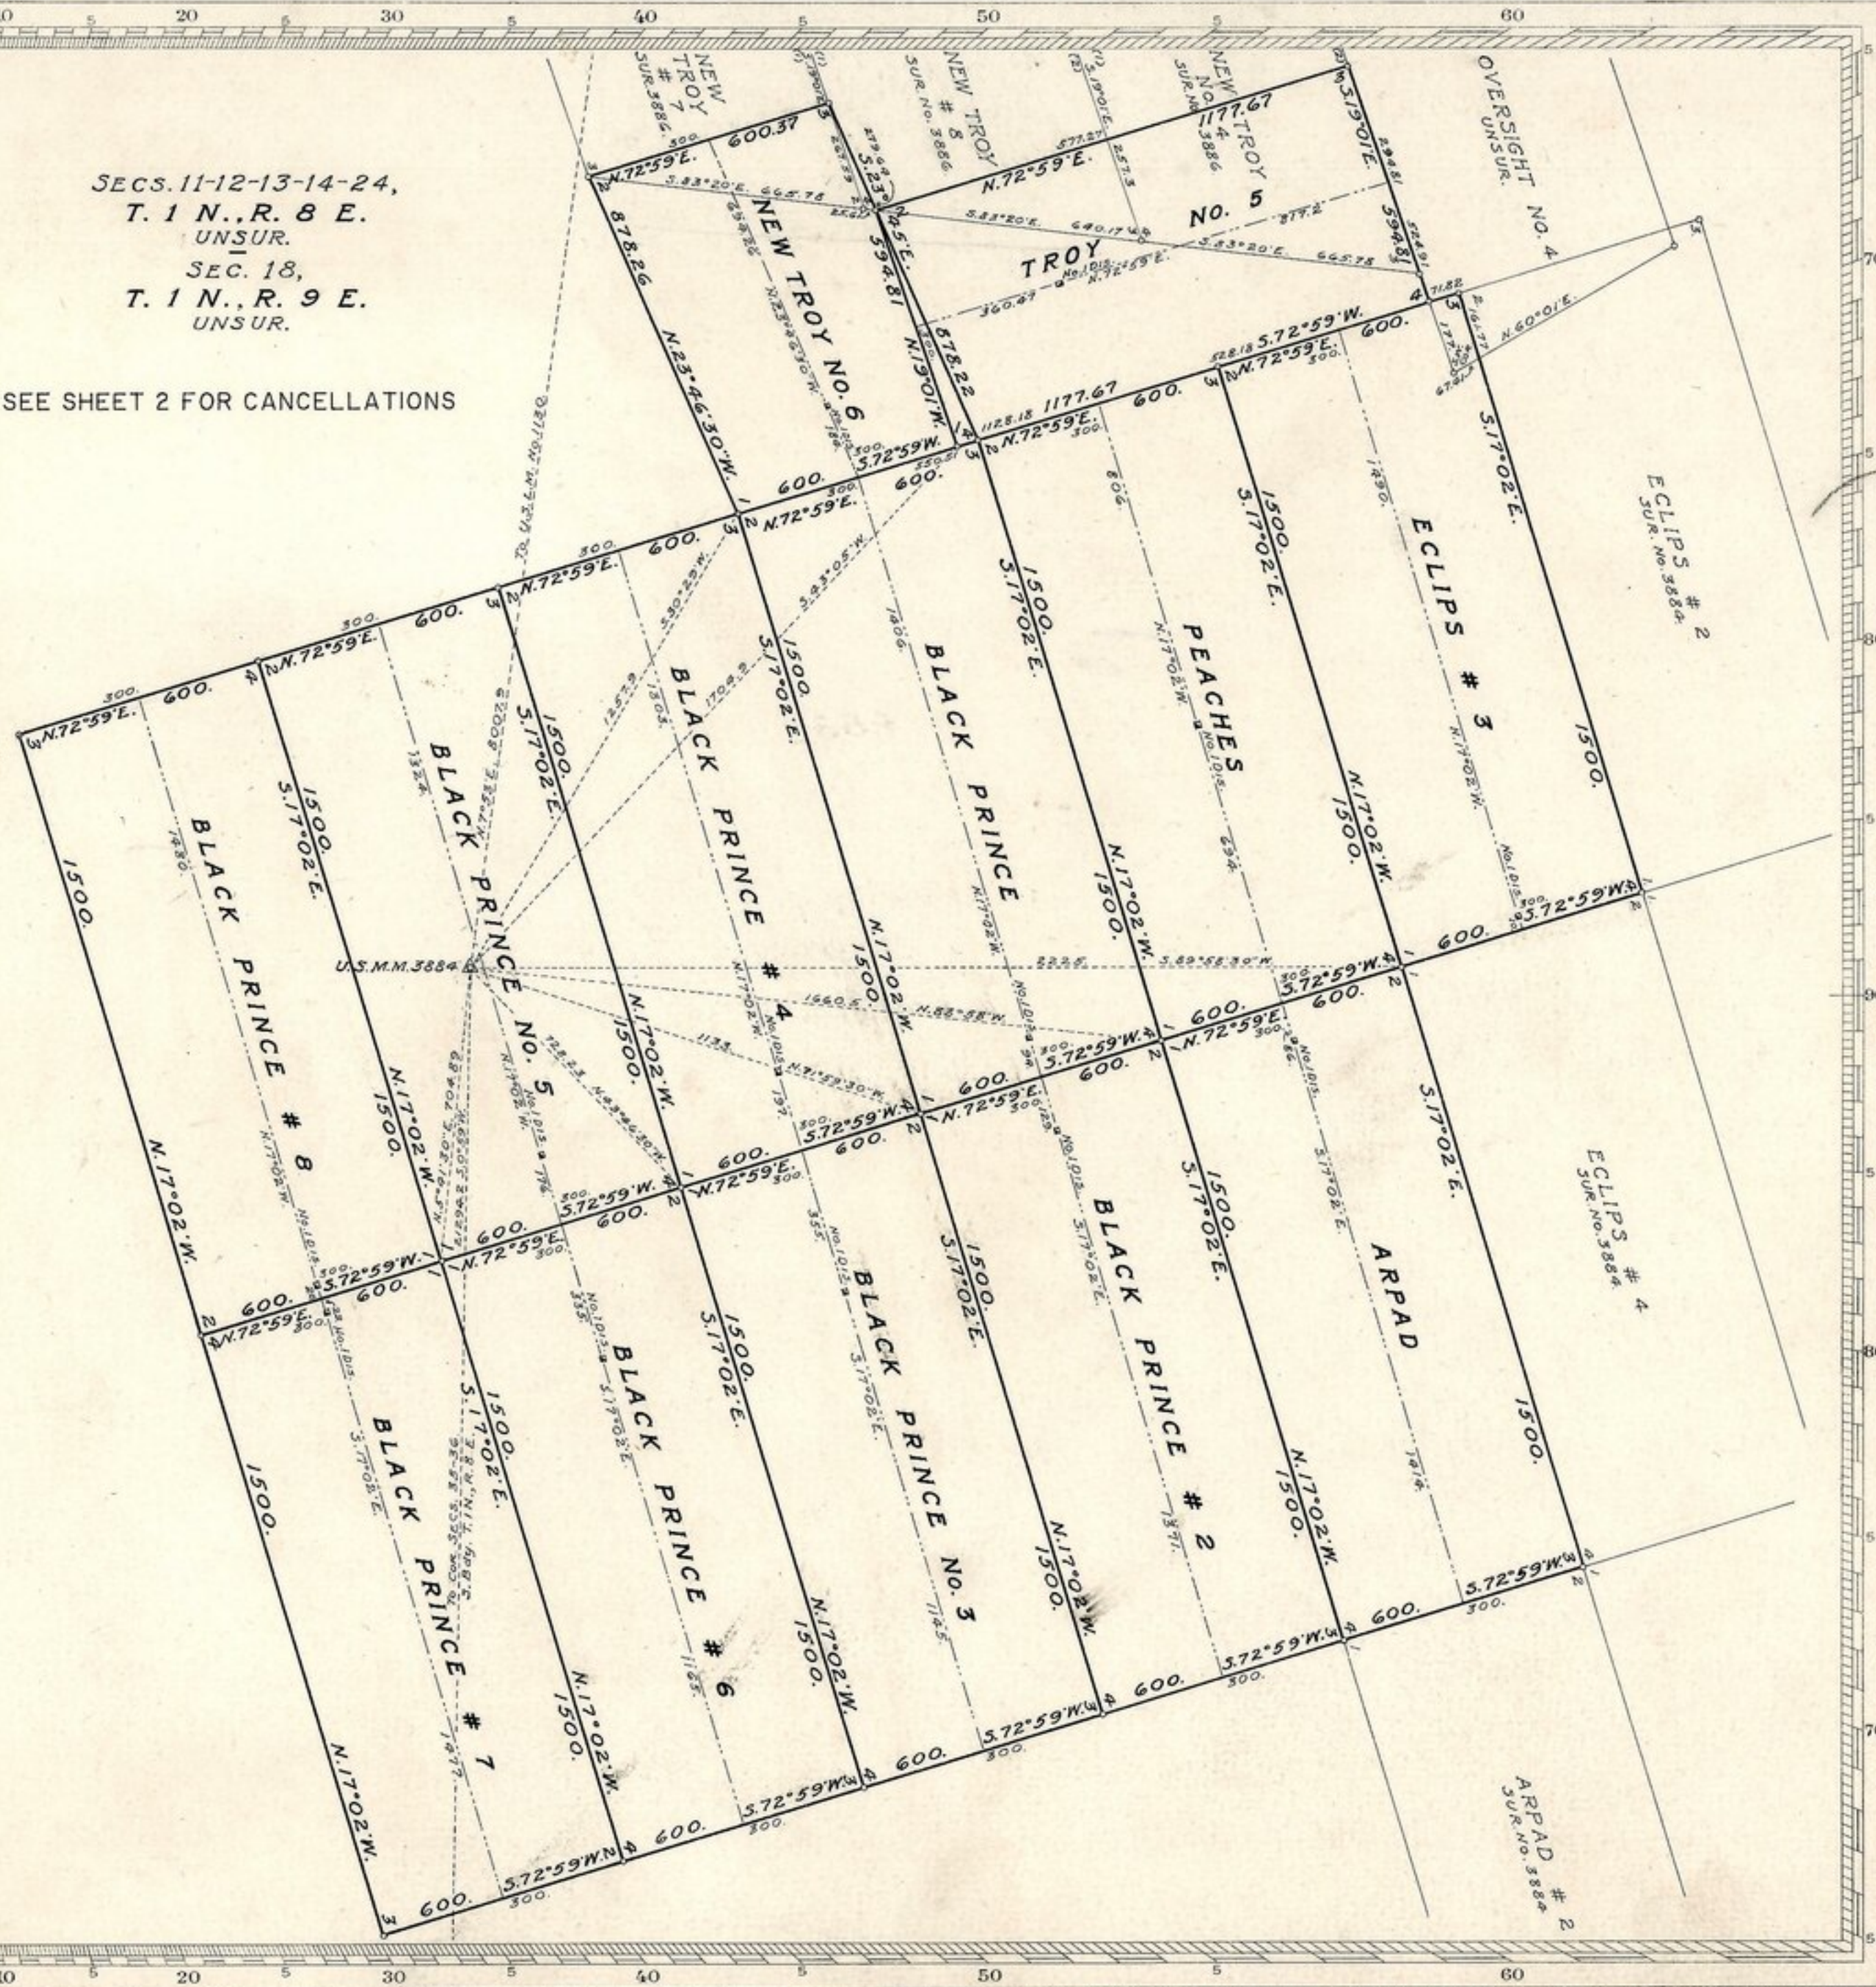

Patent Date
Patent No.
Serial No. -

Claim Located 19

Mineral Survey No. 3884 4-Sheets.

Lot No.
ARIZONA Land District.

PLAT of the claim of

Young Mines Company, Ltd., known as
ARPAD, ARPAD #2, 3, BELLE, BLACK PRINCE, BLACK PRINCE
#2, 4, 6, 7, 8, BLACK PRINCE NOS. 3, 5, DEMOCRAT, ECLIPSE,
ECLIPS #2, 3, 4, 5, GARRYOWEN, GARRYOWEN #2, GLENGARRY,
PEACHES, POSER, POSER #2, 3, REPUBLIC, ST. LAWRENCE,
STANDARD, STANDARD #2, SUNNY SIDE, SUNNY SIDE NOS.
2, 3, TROY NO. 5, NEW TROY NO. 6, and LITTLE ST.
LAWRENCE lodes

IN Superstition MINING DISTRICT,
Pinal COUNTY, Arizona

Containing an Area of Acres.

Scale of 400 Feet to the inch.

Variation 15° E.

SURVEYED March 12 - April 7 19 23 BY

E. C. Kinderman

U.S. Deputy Mineral Surveyor,

The Original Field Notes of the Survey of the Mining Claim of
Young Mines Company, Ltd.

known as the

ARPAD et al lodes

from which this plat has been made under my direction,
have been examined and approved, and are on file in this Office,
and I hereby certify that they furnish such an accurate descrip-
tion of said Mining Claim as will, if incorporated into a patent,
serve fully to identify the premises, and that such reference is
made therein to natural objects or permanent monuments as
will perpetuate and fix the locus thereof.

I further certify that ^{less than} Five Hundred Dollars worth of labor has
been expended or improvements made upon said Mining Claims
by claimant or its grantors and that
said improvements consist of 42 shafts, 2 cuts, 2
tunnels, and 1 crosscut, total value \$4990.

that the location of said improvements is correctly shown
upon this plat, and that no portion of said labor or improve-
ments has been included in the estimate of expenditures
upon any other claim.

And I further certify that this is a correct plat of said Mining
Claim made in conformity with said original field notes of the
survey thereof, and the same is hereby approved.

U.S. Surveyor General's Office.

Phoenix, Arizona,

December 31, 19 24

Charles M. Donohoe

U.S. Surveyor General for

ARIZONA.